
Sezione A-A'

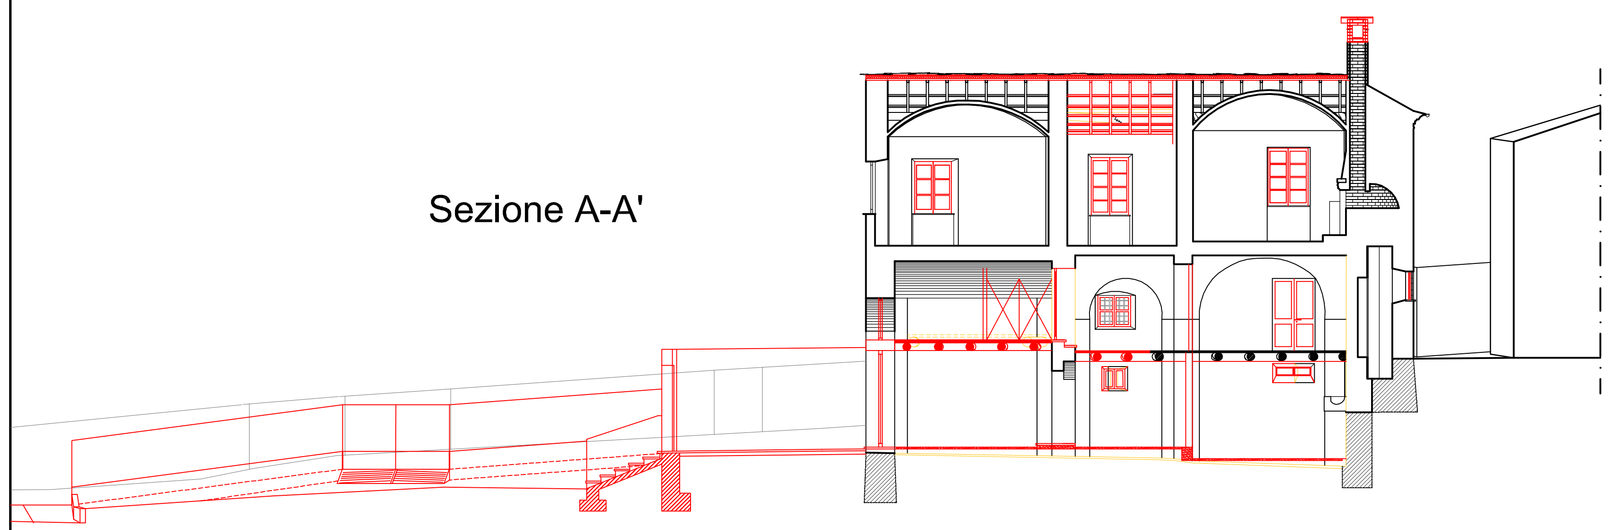

Sezione D-D'



Legenda


Opere in demolizione

Nuove opere

Sezione B-B'




Sezione E-E'

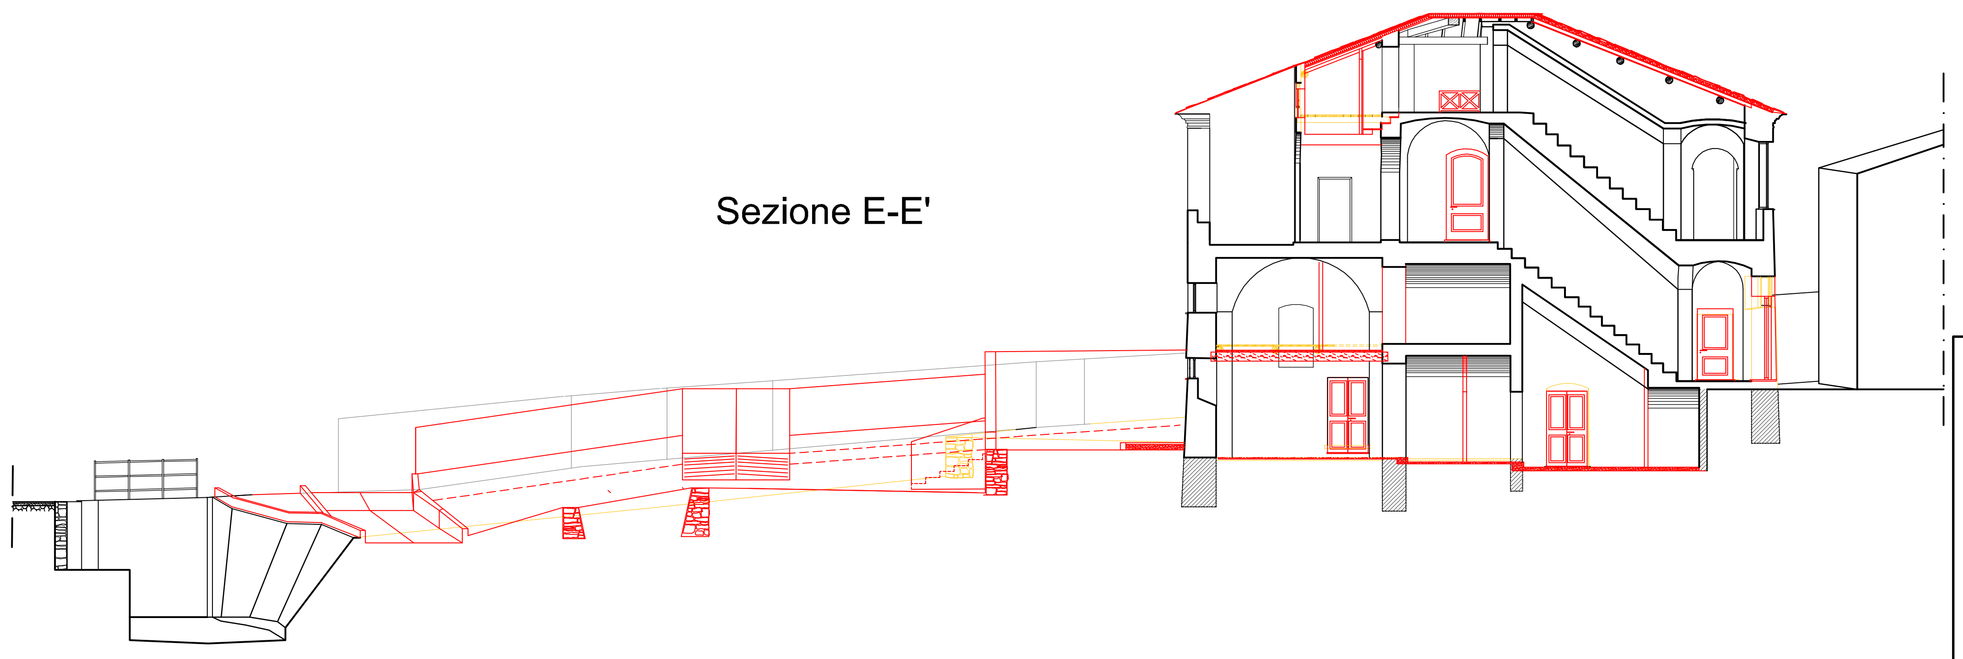

Sezione C-C'



Sezione F-F'

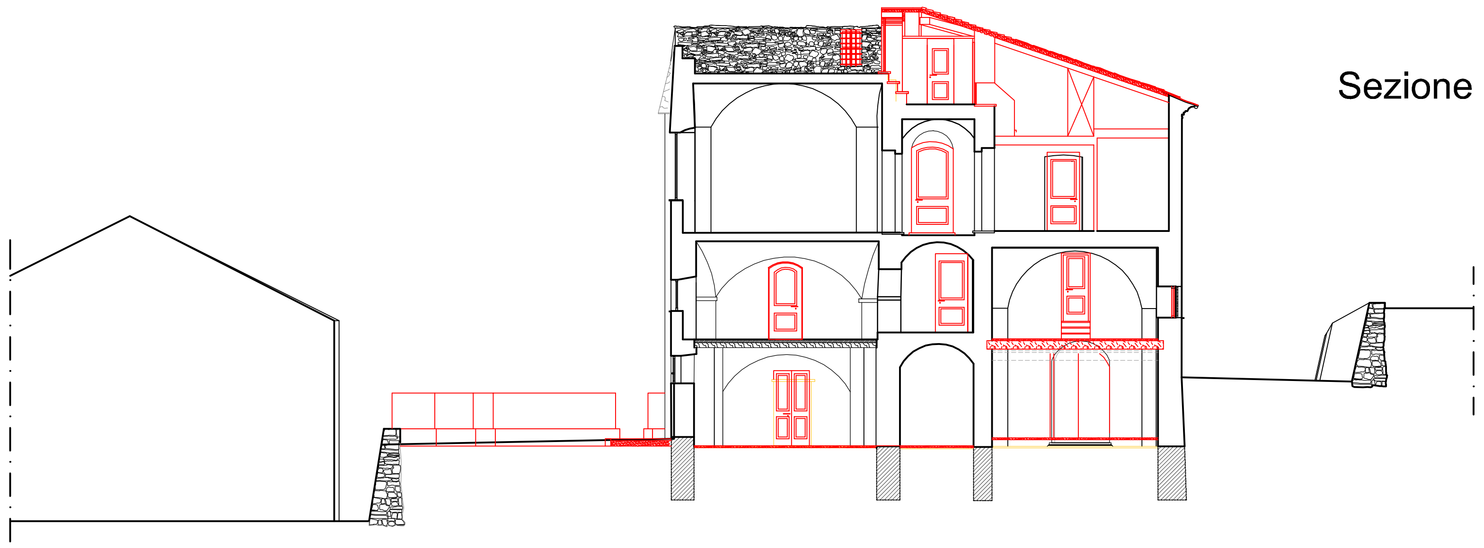

COMUNE DI ARNASCO

(Provincia di Savona)

Ristrutturazione dell'immobile denominato "la torre di Bezzo"

PROGETTO DI RESTAURO

IL COMMITTENTE

IL PROGETTISTA

STUDIO DI ARCHITETTURA "DOTT. ARCH. NICOLA JACOPO PODIO"
Via Genova 123/2 - 17031 Albenga (SV) -
Cod. Fisc. PDO NLJ 68C12 D969Y - Part. IVA 01784520098
Tel 0182-51373 - e.mail: info@studiopodio.it - pec: podio.nicola@pec.it

TAV. N. 14	OGGETTO: RAFFRONTO Sezioni	data maggio 2022
ALL. N.	COMMITTENTE: PRASLIN S.p.a. Via Zara, 23 20159 MILANO (MI) P.I. 09788030154	scala 1:100

QUESTO ELABORATO E' DI PROPRIETA' DELLO STUDIO ED E' PROTETTO A TERMINE DI LEGGE
PROGRAMMA GRAFICO ALLPLAN DELLA NEMETSCHEK AG