COMUNE DI ARNASCO
(Provincia di Savona)

Ristrutturazione dell'immobile denominato "la torre di Bezzo"

PROGETTO DI RESTAURO

IL COMMITTENTE


IL PROGETTISTA

STUDIO DI ARCHITETTURA "DOTT. ARCH. NICOLA JACOPO PODIO"
Via Genova 123/2 - 17031 Albenga (SV) -
Cod. Fisc. PDO NLJ 68C12 D969Y - Part. IVA 01784520098
Tel 0182-51373 - e.mail: info@studiopodio.it - pec: podio.nicola@pec.it

TAV. N.	OGGETTO: PROGETTO	data
8	Piante	maggio 2022
ALL. N.	COMMITTENTE: PRASLIN S.p.a. Via Zara, 23 20159 MILANO (MI) P.I. 09788030154	scala 1:100


QUESTO ELABORATO E' DI PROPRIETA' DELLO STUDIO ED E' PROTETTO A TERMINE DI LEGGE
PROGRAMMA GRAFICO ALLPLAN DELLA NEMETSCHEK AG

Pianta Piano Terra

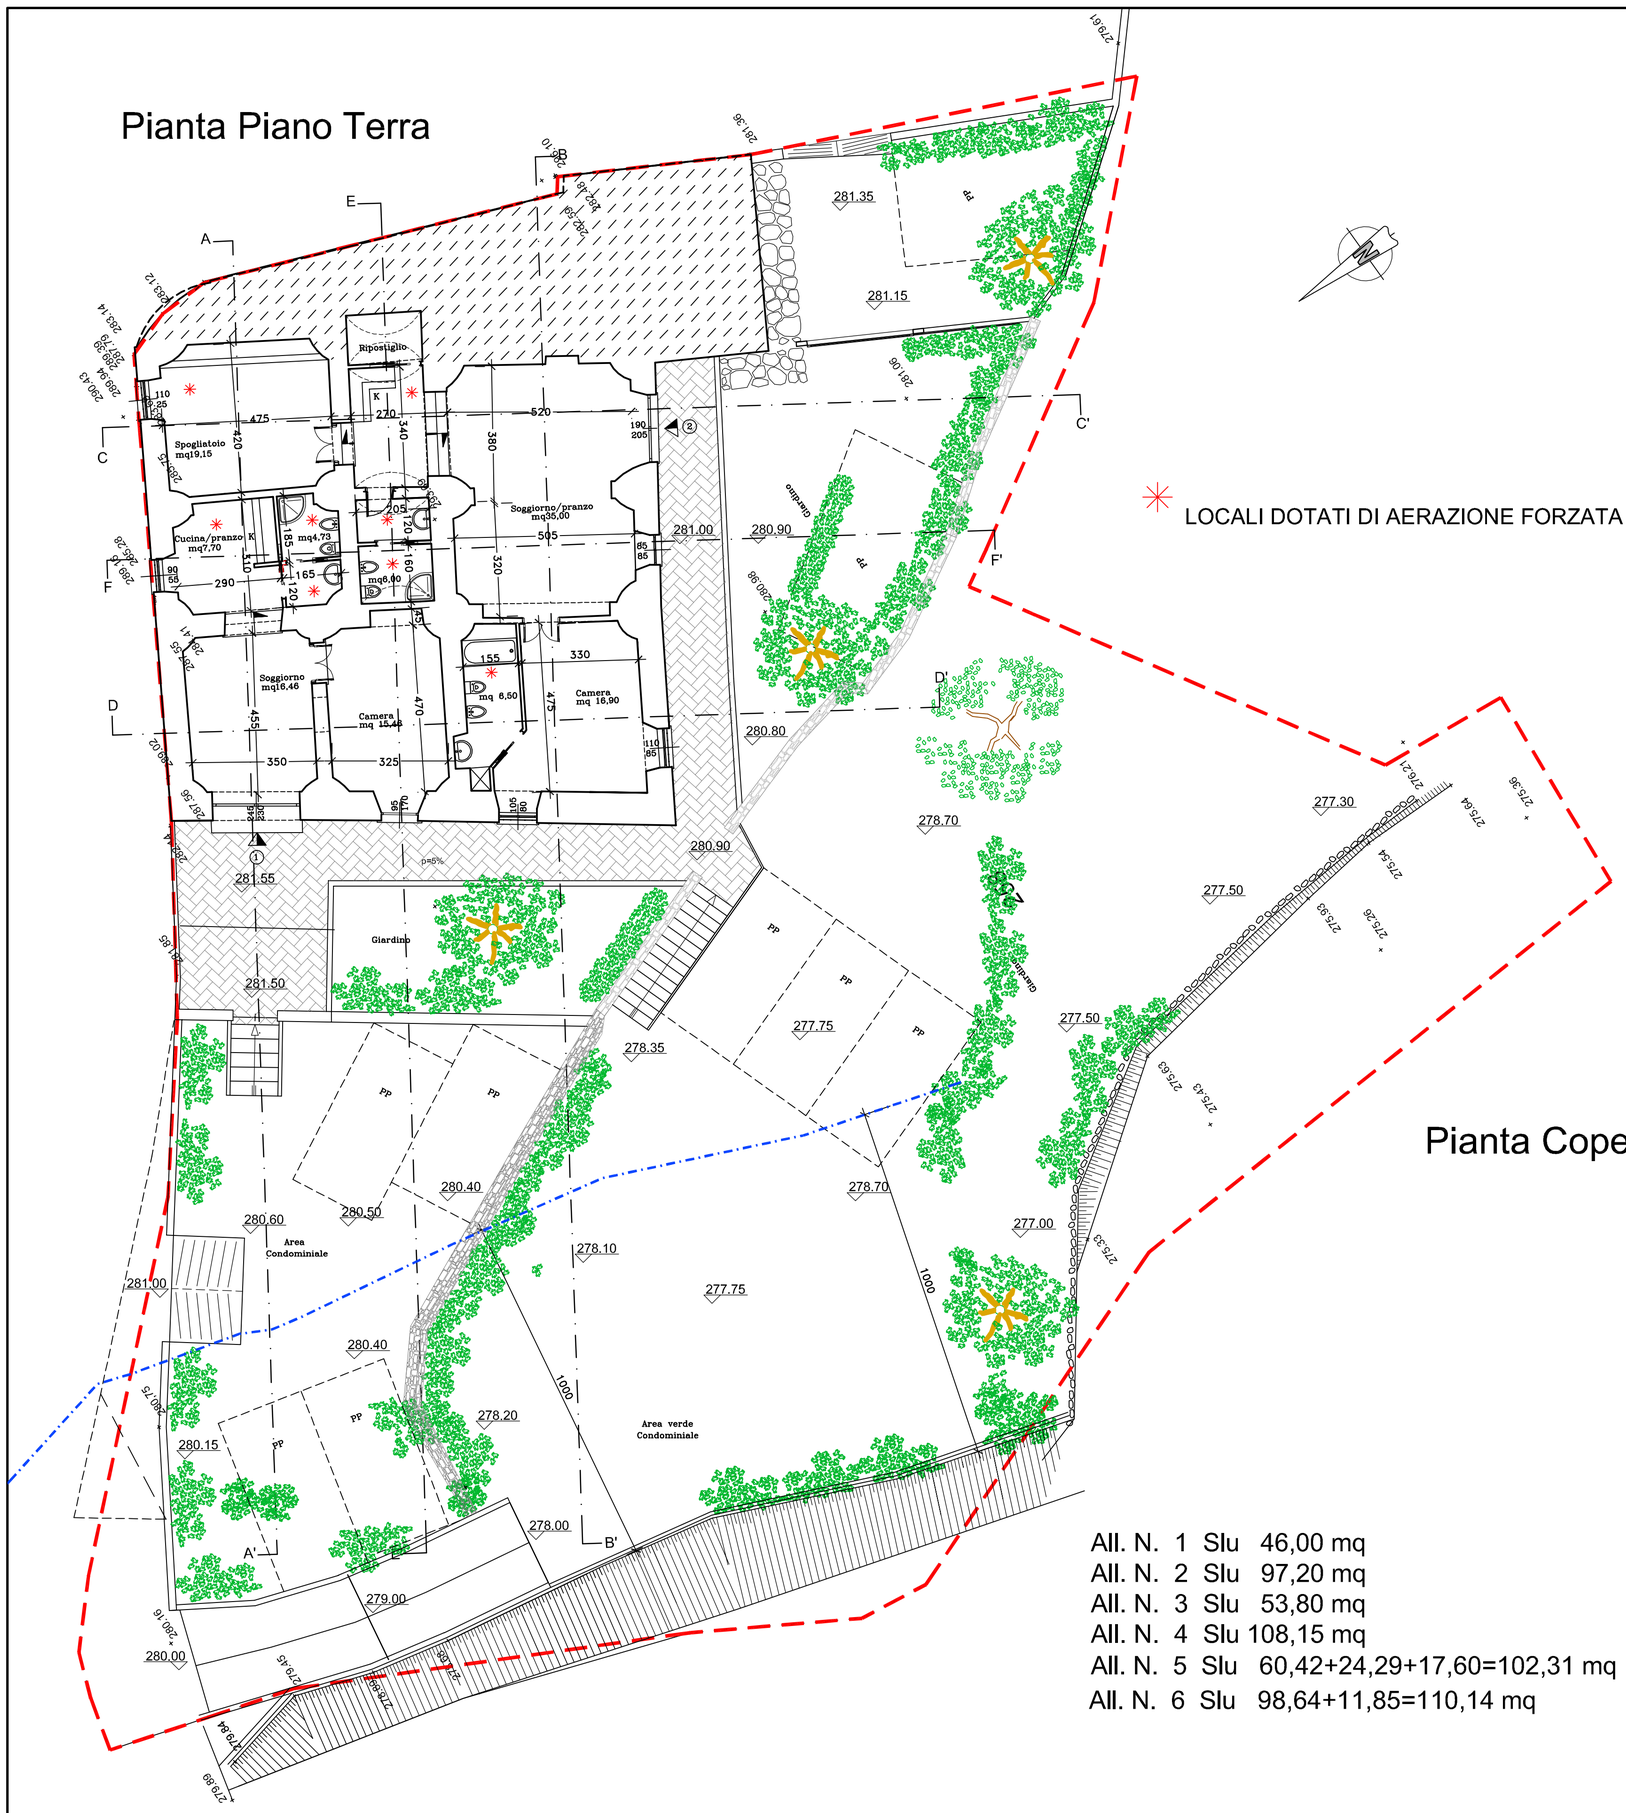


All. N. 1 Slu 46,00 mq
All. N. 2 Slu 97,20 mq
All. N. 3 Slu 53,80 mq
All. N. 4 Slu 108,15 mq
All. N. 5 Slu 60,42+24,29+17,60=102,31 mq
All. N. 6 Slu 98,64+11,85=110,14 mq


Pianta Copertura

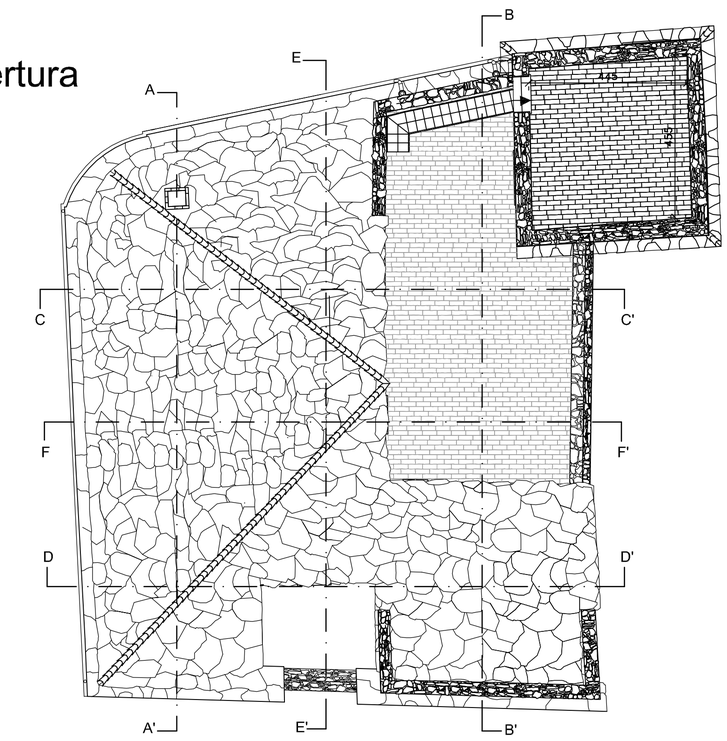

Pianta Piano Primo

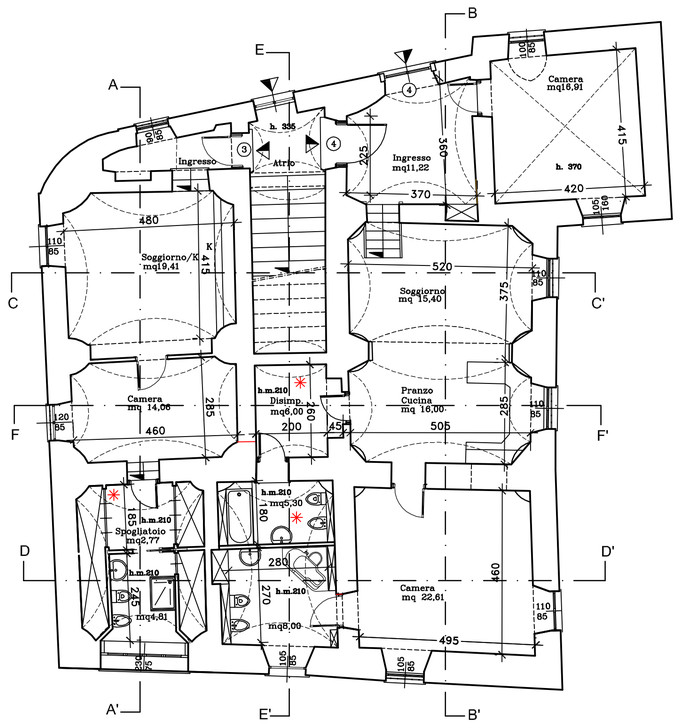

Pianta Piano Secondo

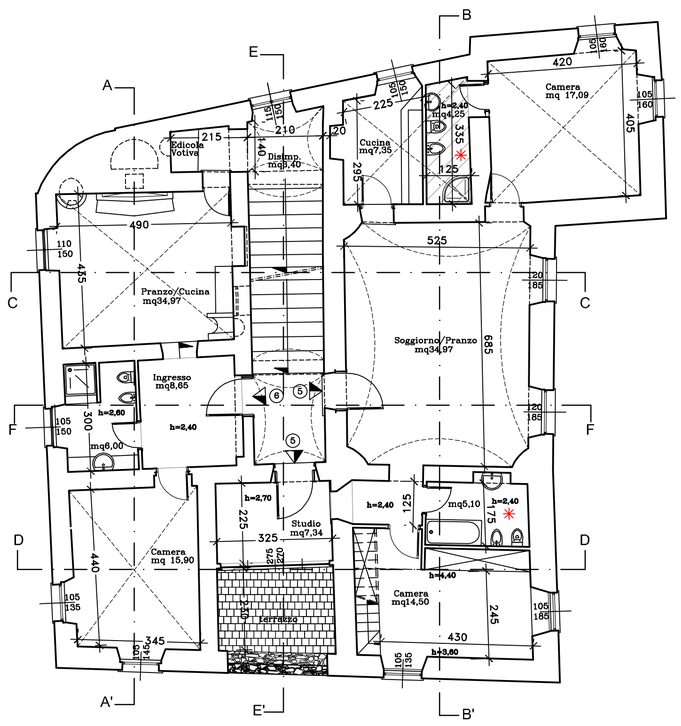

Pianta Piano Terzo

