


prospetto sud

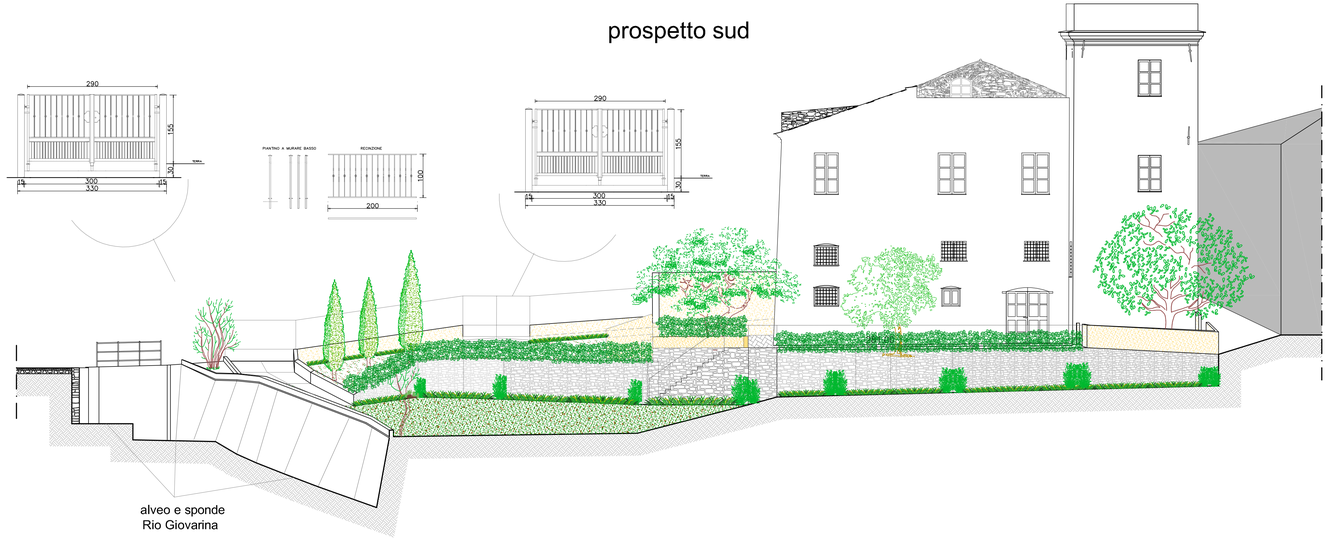

prospetto est

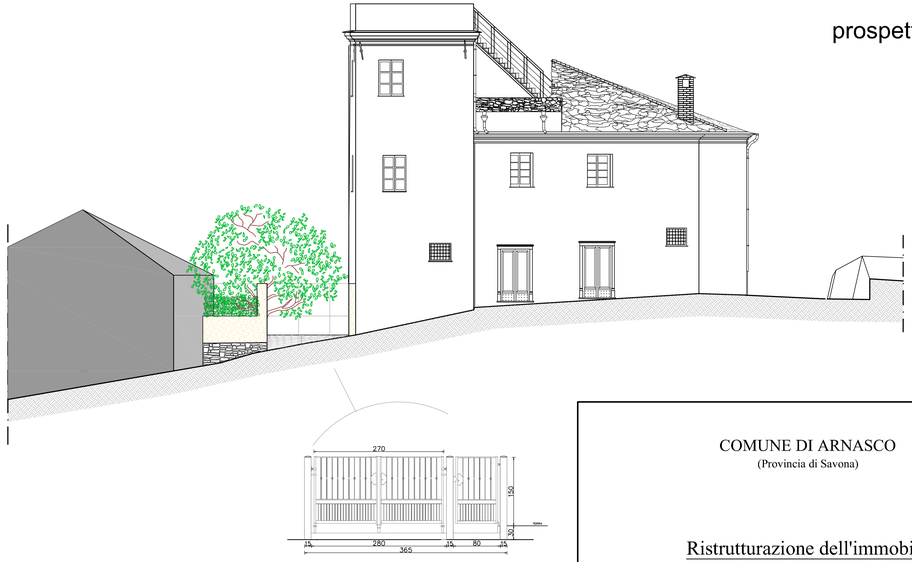

prospetto nord

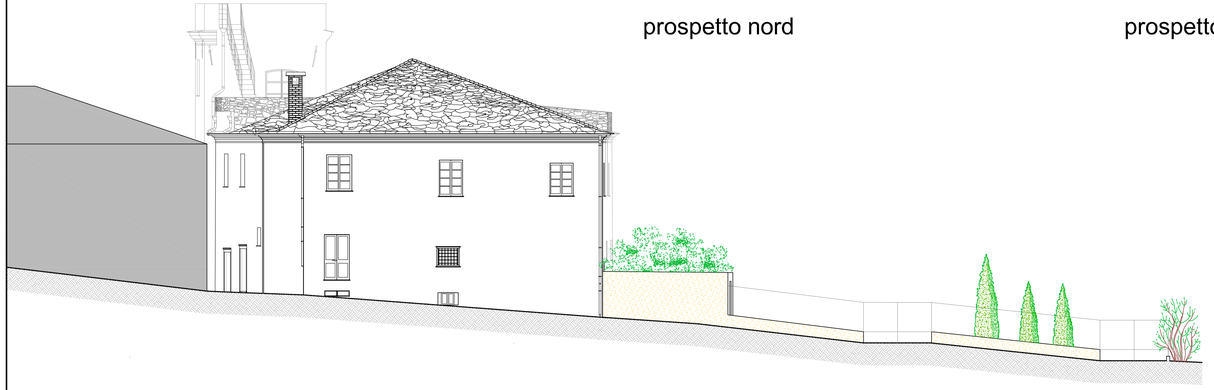

prospetto ovest



COMUNE DI ARNASCO
(Provincia di Savona)

Ristrutturazione dell'immobile denominato "la torre di Bezzo"

PROGETTO DI RESTAURO

IL COMMITTENTE

IL PROGETTISTA

STUDIO DI ARCHITETTURA "DOTT. ARCH. NICOLA JACOPO PODIO"
Via Genova 123/2 - 17031 Albenga (SV) -
Cod. Fisc. PDO NLJ 68C12 D969Y - Part. IVA 0178452098
Tel 0182-51373 - e.mail: info@studiopodio.it - pec: podio.nicola@pec.it

TAV. N.	OGGETTO: PROGETTO	data
9	Prospetti	maggio 2022
ALL. N.	COMMITTENTE: PRASLIN S.p.a. Via Zara, 23 20159 MILANO (MI) P.I. 09788030154	scala 1:100

QUESTO ELABORATO E' DI PROPRIETA' DELLO STUDIO ED E' PROTETTO A TERMINI DI LEGGE
PROGRAMMA GRAFICO ALLPLAN DELLA NEMETSCHEK AG